

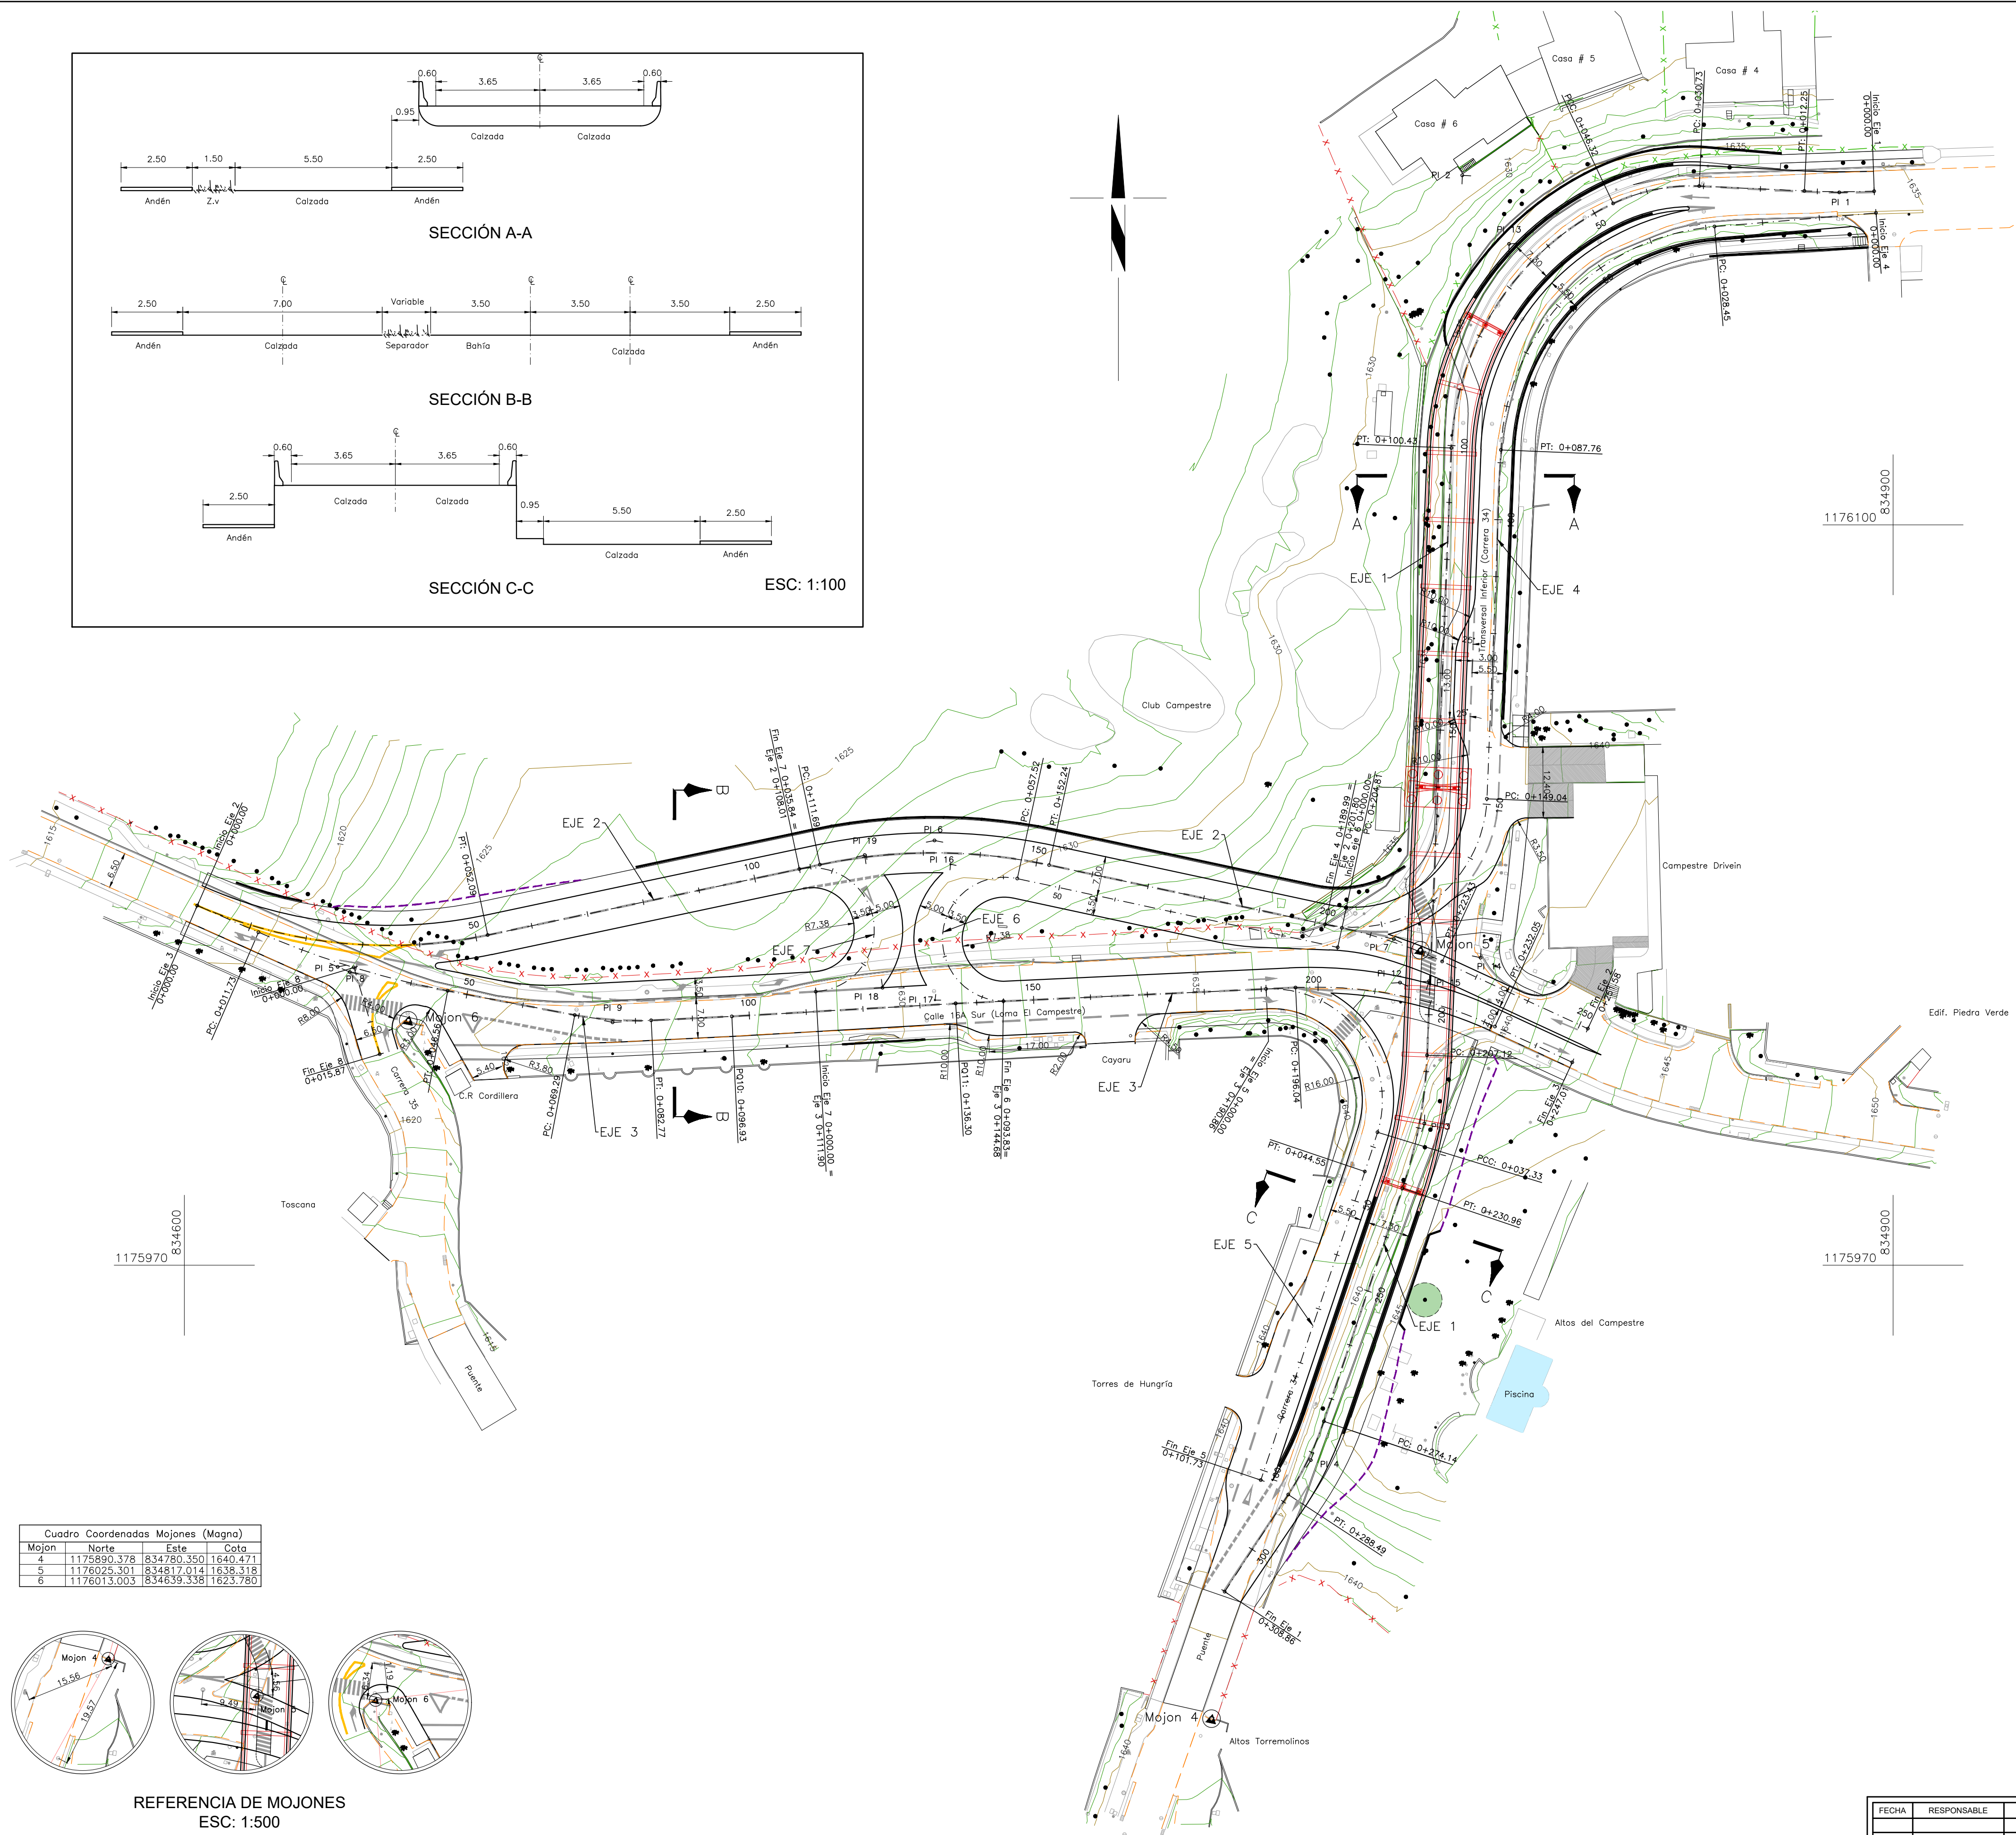


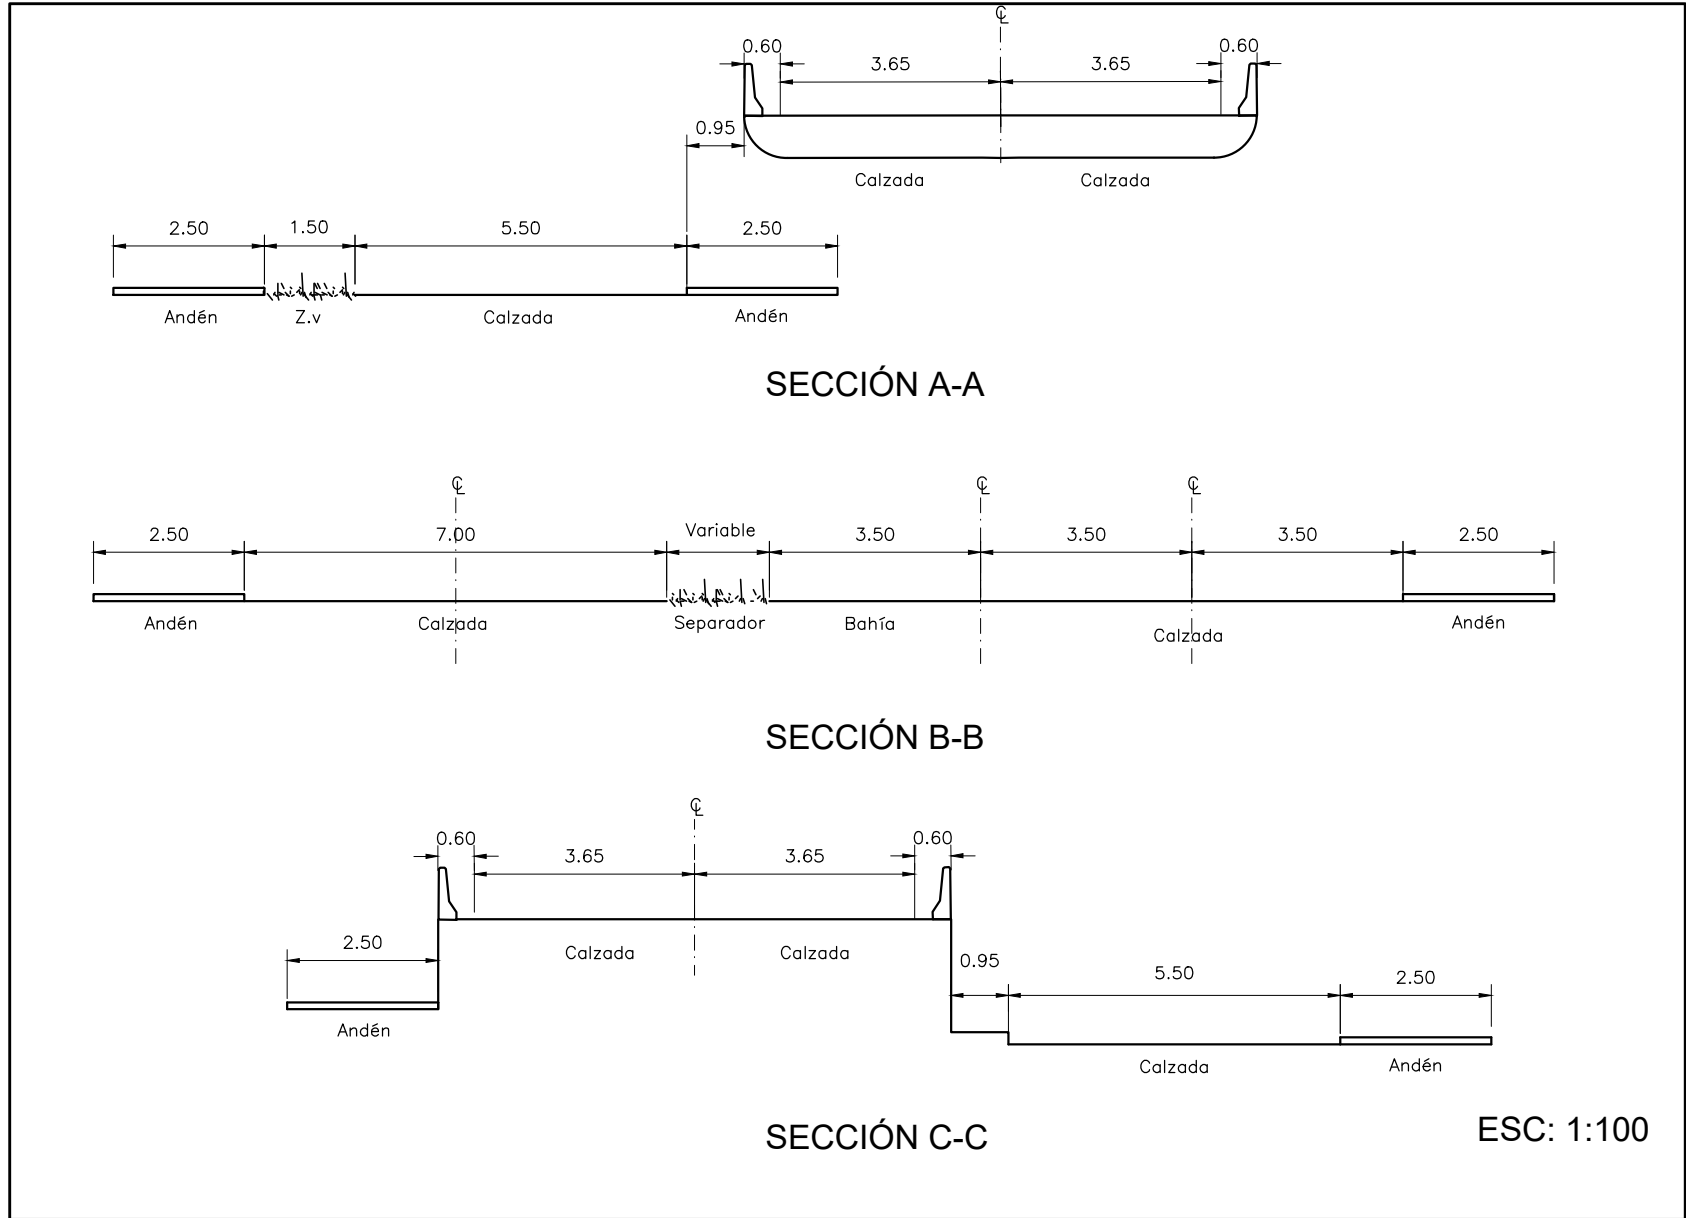

Cuadro Coordenadas Mojones (Magna)			
Mojón	Norte	Este	Cota
4	1175890.378	834780.350	1640.471
5	1176025.301	834817.014	1638.318
6	1176013.003	834639.338	1623.780

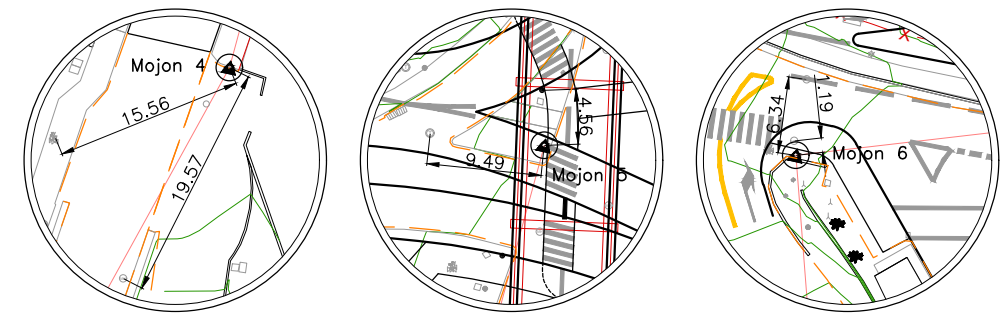

REFERENCIA DE MOJONES
ESC: 1:500

ELEMENTOS DE CURVATURA HORIZONTAL Y COORDENADAS EJE 1													
PUNTO	A	R	T	L	ABSCISAS		AZIMUT	DIST	COORDENADAS		NORTE	ESTE	
					PC	PT			PI - PI				
Inicio					0+000.000	0+012.25	267° 54' 21.55"	6.127		1176158.577	834896.692		
PI 1	04° 40' 40.3425" D	150.00	6.13	12.25	0+000.000	0+012.25	272° 35' 1.88"	66.269		1176158.353	834890.570		
PI 2	90° 17' 48.18" I	32.00	7.95	15.99	0+030.73	0+046.32	182° 17' 13.71"	166.590		1176161.341	834824.368		
PI 3	16° 21' 52.2480" D	83.50	12.01	23.85	0+207.12	0+230.96	198° 39' 05.96"	62.388		1175994.684	834817.720		
PI 4	14° 33' 03.4858" D	56.50	7.21	14.35	0+274.14	0+288.49	213° 12' 09.44"	27.579		1175935.763	834797.764		
Fin					0+308.890					1175912.687	834782.662		

ELEMENTOS DE CURVATURA HORIZONTAL Y COORDENADAS EJE 2													
PUNTO	Δ	R	T	L	ABSCISAS		AZIMUT	DIST	COORDENADAS		NORTE	ESTE	
					PC	PT			PI - PI				
Inicio					0+000.000		113° 34' 18.87"	26.916		1176033.153	834602.279		
PI 5	35° 32' 00.1942" I	84.00	26.92	52.10	0+000.000	0+052.09	78° 02' 18.68"	107.090		1176022.389	834626.949		
PI 6	24° 04' 40.0512" D	96.50	20.98	40.95	0+111.89	0+162.24	102° 06' 58.73"	82.496		1176044.584	834731.714		
PI 7	12° 41' 52.1121" D	84.00	9.35	18.62	0+204.81	0+223.43	114° 48' 50.84"	37.497		1176027.269	834813.372		
Fin					0+251.980					1176011.532	834846.407		

ELEMENTOS DE CURVATURA HORIZONTAL Y COORDENADAS EJE 3													
PUNTO	A	R	T	L	ABSCISAS		AZIMUT	DIST	COORDENADAS		NORTE	ESTE	
					PC	PT			PI-PI				
Inicio					0+000.000		113° 34' 18.87"	29.218		1176033.153	834602.279		
PI 8	12° 45' 10.2834" I	156.50	17.49	34.83	0+011.731	0+046.58	100° 49' 08.59"	46.898		1176021.469	834629.059		
PI 9	13° 40' 11.1742" I	66.50	6.77	13.48	0+069.28	0+082.77	87° 09' 57.42"	20.833		1176012.648	834675.211		
PQ 10	00° 28' 28.66" I				0+096.930	88° 42' 28.76"	39.371		1176013.690	834696.118			
PQ 11	00° 36' 9.30" D				0+136.300	87° 18' 38.06"	78.098		1176015.951	834735.424			
PI 12	27° 30' 12.7867" D	75.00	18.36	36.00	0+196.04	0+232.05	114° 48' 50.84"	33.319		1176019.615	834813.436		
Fin					0+247.010					1176005.632	834843.679		

ELEMENTOS DE CURVATURA HORIZONTAL Y COORDENADAS EJE 4													
PUNTO	A	R	T	L	ABSCISAS		AZIMUT	DIST	PI - PI	COORDENADAS			
					PC	PT				NORTE	ESTE		
Inicio					0+000.000		265° 10' 21.19"	64.651		1176154.746	834897.016		
PI 13	82° 53' 07.4773" I	41.00	36.20	59.31	0+028.45	0+087.76	182° 17' 13.71"	125.403		1176149.305	834832.594		
PI 14	99° 49' 45.0210" D	23.50	27.92	40.95	0+149.04	0+189.99	282° 6' 58.73"	27.922		1176024.002	834827.590		
Fin					0+189.990					1176028.862	834800.290		

ELEMENTOS DE CURVATURA HORIZONTAL Y COORDENADAS EJE 5													
PUNTO	Δ	R	T	L	ABSCISAS		AZIMUT	DIST	COORDENADAS				
					PC	PT			PI - PI	NORTE	ESTE		
Inicio					0+000.000		87° 18' 38.06"	28.658	1176018.511	834789.923			
PI 15	111° 20' 27.90" D	19.50	27.68	37.33	0+000.000 0+037.33		198° 39' 5.96"	92.426	1176019.855	834818.550			
		249.30	3.61	7.23	0+037.33 0+044.55								
Fin					0+101.730				1175932.284	834788.991			

ELEMENTOS DE CURVATURA HORIZONTAL Y COORDENADAS EJE 6													
PUNTO	A	R	T	L	ABSCISAS		AZIMUT	DIST	COORDENADAS				
					PC	PT			PI - PI	NORTE	ESTE		
Inicio					0+000.000		282° 06' 58.73"	69.521		1176025.808	834802.459		
PI 16	95° 35' 59.75" I	10.88	11.99	18.15	0+057.52	0+075.68	186° 30' 58.99"	23.998		1176040.401	834734.526		
PI 17	95° 35' 59.75" I	10.88	11.99	18.15	0+075.68	0+093.83	90° 54' 59.24"	11.999		1176016.558	834731.803		
Fin					0+093.830					1176016.366	834743.800		

ELEMENTOS DE CURVATURA HORIZONTAL Y COORDENADAS EJE 7													
PUNTO	A	R	T	L	ABSCISAS		AZMUT	DIST	COORDENADAS				
					PC	PT			PI - PI	NORTE	ESTE		
Inicio					0+000.000		86° 42' 28.76"	11.740		1176018.044	834710.866		
PI 18	94° 20' 5.04" I	10.88	11.74	17.92	0+000.000	0+017.92	352° 22' 23.72"	23.480		1176018.718	834722.587		
PI 19	94° 20' 5.04" I	10.88	11.74	17.92	0+017.92	0+035.84	258° 2' 18.68"	11.740		1176041.990	834715.470		
Fin					0+035.840					1176039.557	834707.985		

ELEMENTOS DE CURVATURA HORIZONTAL Y COORDENADAS EJE 8													
PUNTO	A	R	T	L	ABSCISAS		AZIMUT	DIST	PI - PI	COORDENADAS			
					PC	PT					NORTE	ESTE	
Inicio					0+000.000		163° 20' 45.85"	15.873		1176022.267		834629.775	
Fin					0+015.870					1176007.060		834634.324	

CONVENCIONES PLANTA

- Borde vía existente
- Eje diseño
- Borde vía
- Curvas redondas
- Curvas intermedias
- Cerramiento
- Cerco vivo
- Chalhan de corte
- Mojón



SECRETARÍA DE
INFRAESTRUCTURA FÍSICA

PROYECTO: MADURACION DE ESTUDIOS PARA EL MEJORAMIENTO VIAL DE LA INTERSECCION UBICADA EN LA CARRERA 34 -TRANSVERSAL INFERIOR- CON LA CALLE 16A SUR EN LA CIUDAD DE MEDELLIN

CONTIENE: PLANTA

ELABORADO: ALVARO VELEZ GIL	CONTRATISTA: VÍAS Y TRÁNSITO S.A.S
DISEÑO ARQUITECTONICO:	NÚMERO DE CONTRATO: 315-2018 CON EMPRESA DESARROLLO URBANO
DISEÑO ESTRUCTURAL:	ESCALA: 1:500
DISEÑO ELECTRICO:	FECHA: DICIEMBRE 2018
DISEÑO HIGIENIZANTE:	01

12